
FRONT ELEVATION (EXTERNAL VIEW)

SCALE 1:40

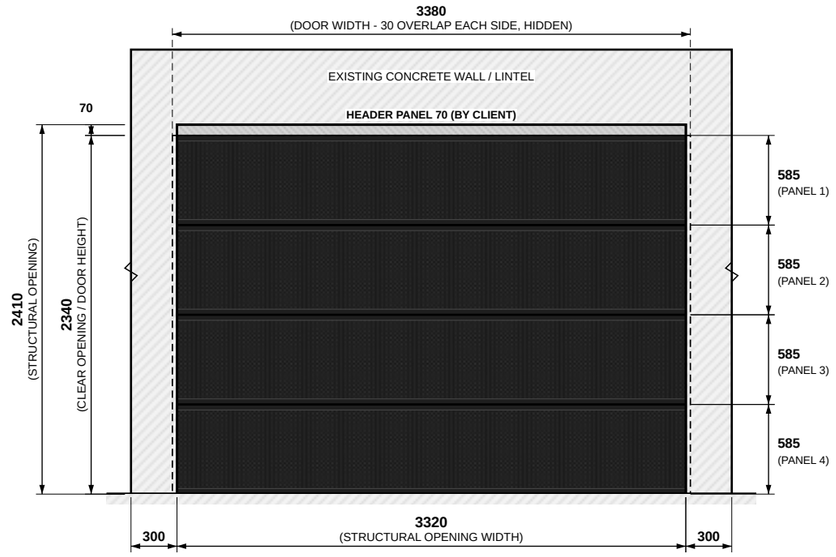


PLAN VIEW (LOOKING UP TO CEILING)


SCALE 1:40

SIDE SECTION (THROUGH OPENING)

SCALE 1:25

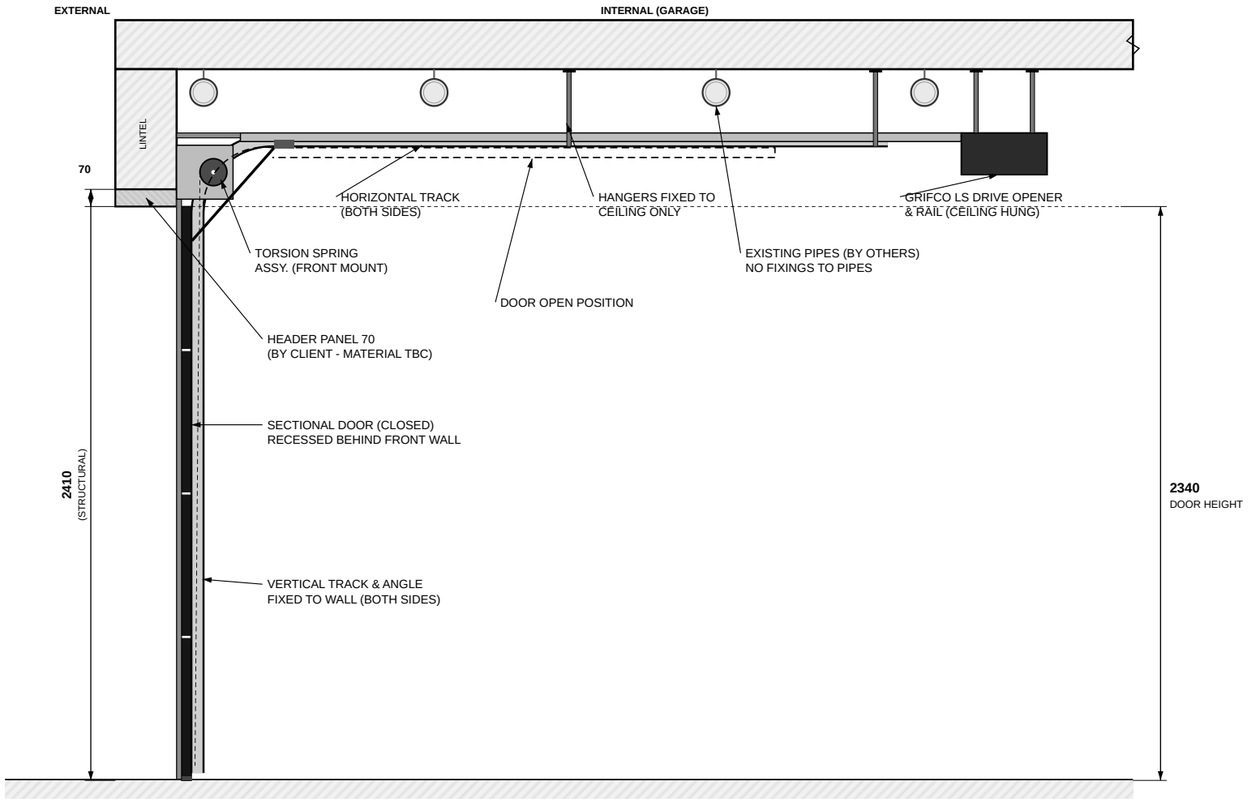

PERFORATION DETAIL (SCALE 1:1)

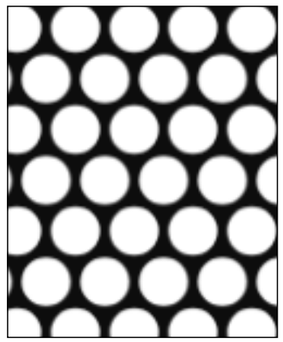

PERFTECH P7995 - ROUND HOLE (60° STAGGERED)

Hole Diameter:	7.95 mm
Pitch:	9.53 mm
Open Area:	62% (nominal)
Finish:	Black powder coat
Panels:	4 x 585 mm

DOOR SCHEDULE

ITEM	SIZE (mm)	REMARK
Structural opening (W x H)	**3320 x 2410**	
Header panel	**70**	BY CLIENT
Clear opening (W x H)	**3320 x 2340**	
Door size (W x H)	**3380 x 2340**	
Overlap each side	**30**	BEHIND WALL
Door edge to side wall	**270**	EACH SIDE
Panels	**4 x 585**	
Mounting	**Recessed**	INTERNAL FACE
Operator	**Grifco LS Drive**	CEILING HUNG

SPECIFICATIONS

Door Type:	Sectional Garage Door (Perforated Panels)
Structural Opening:	3,320 W x 2,410 H mm
Header Panel:	70 mm (by client, material TBC)
Clear Opening:	3,320 W x 2,340 H mm
Door Size:	3,380 W x 2,340 H mm
Overlap / Side Room:	30 mm each side / 270 mm each side
Panels:	4 No. x 585 mm high
Track:	Standard lift (by manufacturer)
Colour / Finish:	Black (powder coat)

MOTOR

Model:	Grifco LS Drive
Location:	Ceiling mounted, rear centre
Support:	Hangers fixed to ceiling
	(no fixing to pipes)
Power Supply:	By others
Electrician:	TBD (confirm with supplier)

NOTES

1. All dimensions in millimetres (mm). Do not scale - use figured dimensions.
2. Structural opening 3,320 W x 2,410 H. Header panel 70 mm by client (material TBC).
3. Clear opening after header panel: 3,320 W x 2,340 H.
4. Door 3,380 W x 2,340 H installed on internal face of front wall (recessed).
5. Door overlaps opening by 30 mm each side; 270 mm from door edge to side walls.
6. Tracks, hangers and opener fixed to ceiling / walls only. Nothing fixed to existing pipes.
7. Perforated panels: Perftech P7995, black powder coat, interior & exterior.
8. Drawing for builder coordination. Final details to be confirmed by door manufacturer.

PROJECT:	**GARAGE DOOR SHOP DRAWING**
ADDRESS:	**118 Glass St, Essendon VIC 3040**
JOB No.:	207904
DATE:	05 NOVEMBER 2026
SCALE:	AS SHOWN @ A3
REVISION:	F - REDRAWN TO SITE OPENING
DRAWING No.:	**GD-01 SHEET: 1 OF 1**