

FRONT ELEVATION (INTERNAL VIEW)

SCALE 1:40 - VIEWED FROM INSIDE

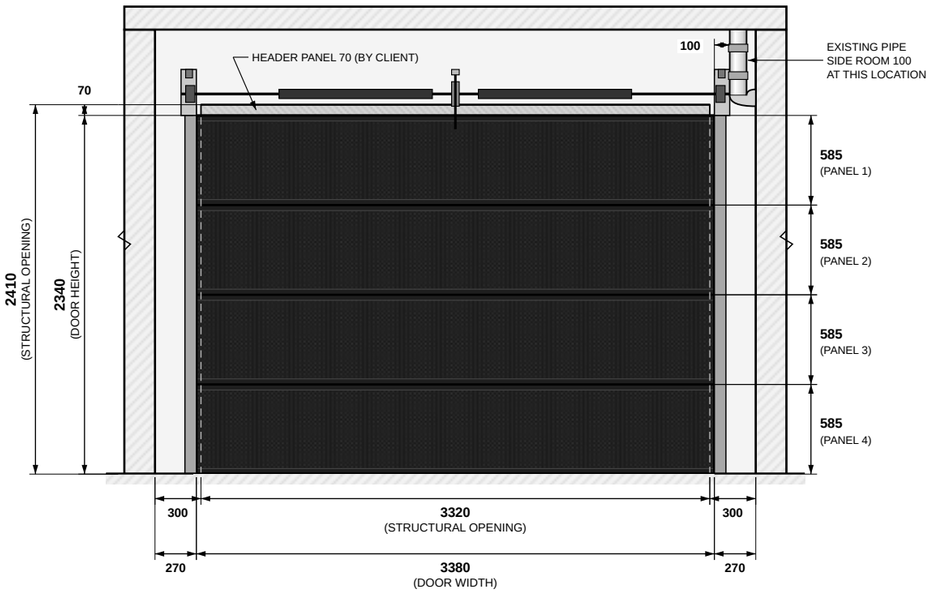


PLAN VIEW (TOP VIEW)

SCALE 1:40

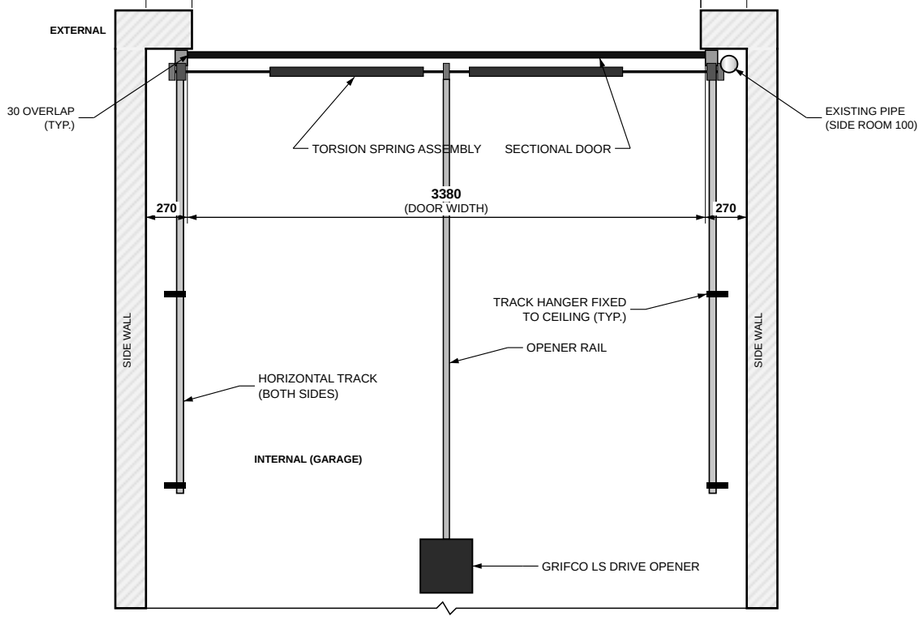


SIDE SECTION (THROUGH OPENING)

SCALE 1:25

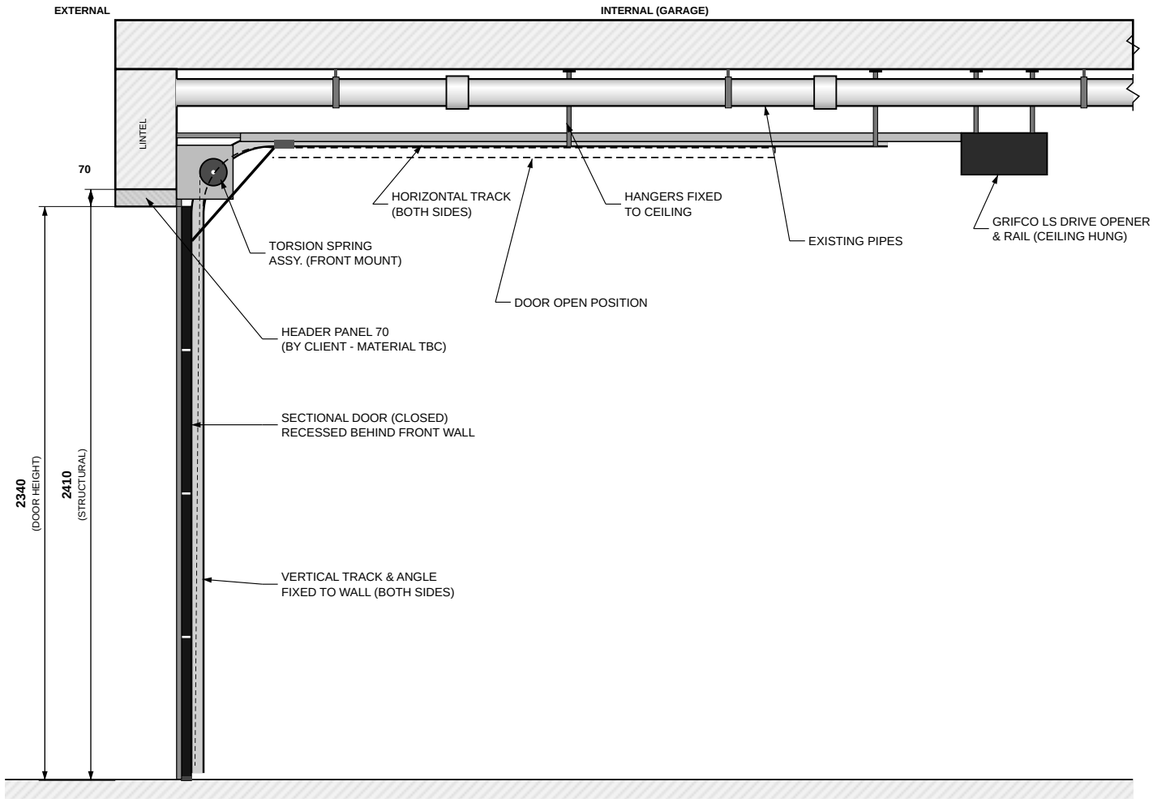

PERFORATION DETAIL (SCALE 1:1)

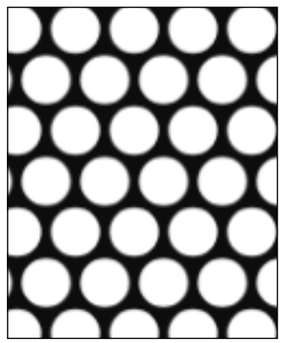

PERFTECH P7995 - ROUND HOLE (60° STAGGERED)

Hole Diameter:	7.95 mm
Pitch:	9.53 mm
Open Area:	62% (nominal)
Finish:	Black powder coat
Panels:	4 x 585 mm

DOOR SCHEDULE

ITEM	SIZE (mm)	REMARK
Structural opening (W x H)	**3320 x 2410**	
Header panel	**70**	BY CLIENT
Clear opening (W x H)	**3320 x 2340**	
Door size (W x H)	**3380 x 2340**	
Overlap each side	**30**	BEHIND WALL
Door edge to side wall	**270**	EACH SIDE
Panels	**4 x 585**	
Mounting	**Recessed**	INTERNAL FACE
Operator	**Grifco LS Drive**	CEILING HUNG

SPECIFICATIONS

Door Type:	Sectional Garage Door (Perforated Panels)
Structural Opening:	3,320 W x 2,410 H mm
Header Panel:	70 mm (by client, material TBC)
Clear Opening:	3,320 W x 2,340 H mm
Door Size:	3,380 W x 2,340 H mm
Overlap / Side Room:	30 mm each side / 270 mm each side
Panels:	4 No. x 585 mm high
Track:	Standard lift (by manufacturer)
Colour / Finish:	Black (powder coat)

MOTOR

Model:	Grifco LS Drive
Location:	Ceiling mounted, rear centre
Support:	Hangers fixed to ceiling
Power Supply:	By client, at rear centre
	(motor location)

NOTES

1. All dimensions in millimetres (mm). Do not scale - use figured dimensions.
2. Structural opening 3,320 W x 2,410 H. Header panel 70 mm by client (material TBC).
3. Clear opening after header panel: 3,320 W x 2,340 H.
4. Door 3,380 W x 2,340 H installed on internal face of front wall (recessed).
5. Door overlaps opening by 30 mm each side; 270 mm from door edge to side walls.
6. Existing pipe at RH internal corner reduces side room to 100 mm locally (see front elevation).
7. Client to supply power at rear centre of garage (motor location).
8. Perforated panels: Perftech P7995, black powder coat, interior & exterior.
9. Drawing for builder coordination. Final details to be confirmed by door manufacturer.

PROJECT:	**GARAGE DOOR SHOP DRAWING**
ADDRESS:	**118 Glass St, Essendon VIC 3040**
JOB No.:	207904
DATE:	05 NOVEMBER 2026
SCALE:	AS SHOWN @ A3
REVISION:	F - REDRAWN TO SITE OPENING
DRAWING No.:	**GD-01 SHEET: 1 OF 1**