
FRONT ELEVATION (EXTERNAL VIEW)

SCALE 1:40

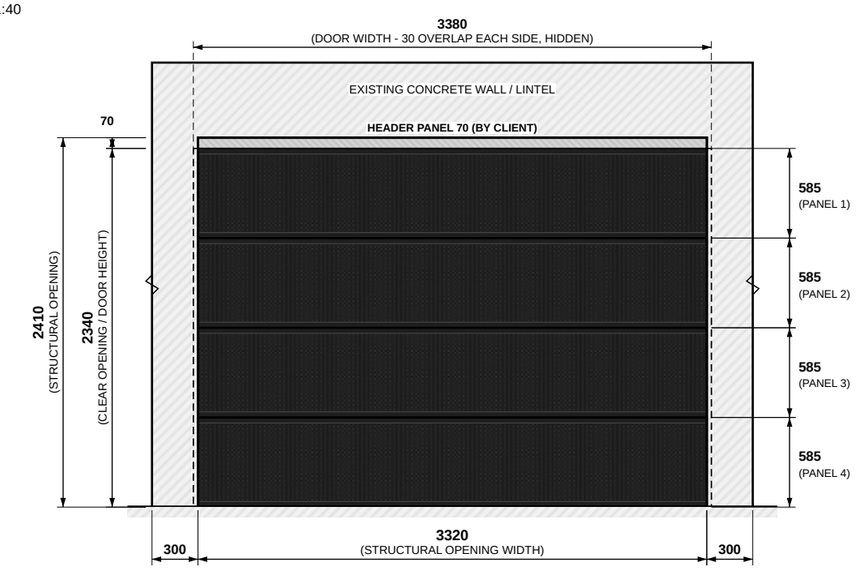


PLAN VIEW (TOP VIEW)


SCALE 1:40

SIDE SECTION (THROUGH OPENING)

SCALE 1:25

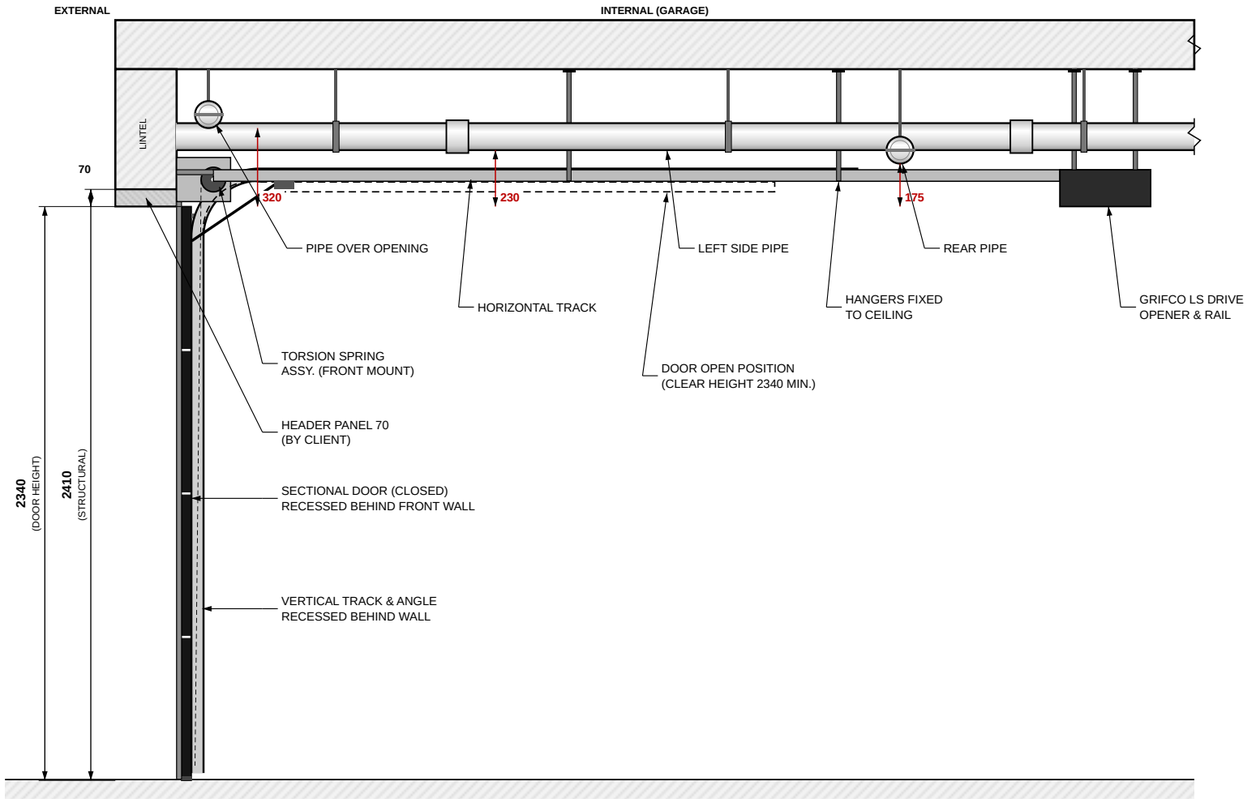

PERFORATION DETAIL (SCALE 1:1)

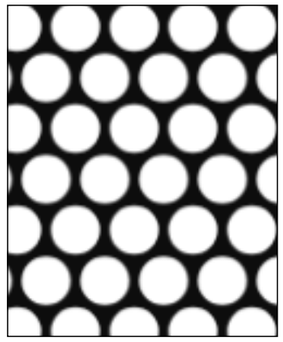

PERFTECH P7995 - ROUND HOLE (60° STAGGERED)

Hole Diameter:	7.95 mm
Pitch:	9.53 mm
Open Area:	62% (nominal)

MOTOR

Model:	Grifco LS-Drive GLD-SDO-R2.5M
Duty:	50 cycles/day - suits 6-car parking
Door Limits:	160 kg max. / 15 m² max. (door 7.9 m²)
Size / Location:	3,972 L x 150 H - ceiling, rear centre
Support:	Hangers fixed to ceiling
Power Supply:	230-240 V single phase, 225 W, 10 A GPO
	by client at motor - 3 phase not required
FIP:	Fire OPEN input: N/O dry contact to terminals
	1 (trigger) & 2 (common). Latched signal holds
	door fully open - all other commands ignored

SPECIFICATIONS

Door Type:	Sectional Garage Door (Perforated Panels)
Structural Opening:	2,410 H x 3,320 W mm
Header Panel:	70 mm (by client)
Clear Opening:	2,340 H x 3,320 W mm
Door Size:	2,340 H x 3,380 W mm
Overlap:	30 mm each side
Panels:	4 No. x 585 mm high
Track:	To suit site headroom (by manufacturer)
Colour / Finish:	Black (powder coat)

NOTES

1. All dimensions in millimetres (mm). Do not scale - use figured dimensions.
2. Door & guides recessed behind front wall - wheels & track approx. 100-150 mm each side of opening.
3. Clear height when door is open: 2,340 mm or higher (door & hardware sit above top of opening).
4. Wall finishes: site manager advised he will inform us if any cover is added to concrete walls.
5. DISCLAIMER: Sizes shown may vary to suit site conditions. Confirm all dimensions on site.

PROJECT:	**GARAGE DOOR SHOP DRAWING**
ADDRESS:	**118 Glass St, Essendon VIC 3040**
JOB No.:	207904
DATE:	05 NOVEMBER 2026
SCALE:	AS SHOWN @ A3
REVISION:	F - REDRAWN TO SITE OPENING
DRAWING No.:	**GD-01 SHEET: 1 OF 1**